

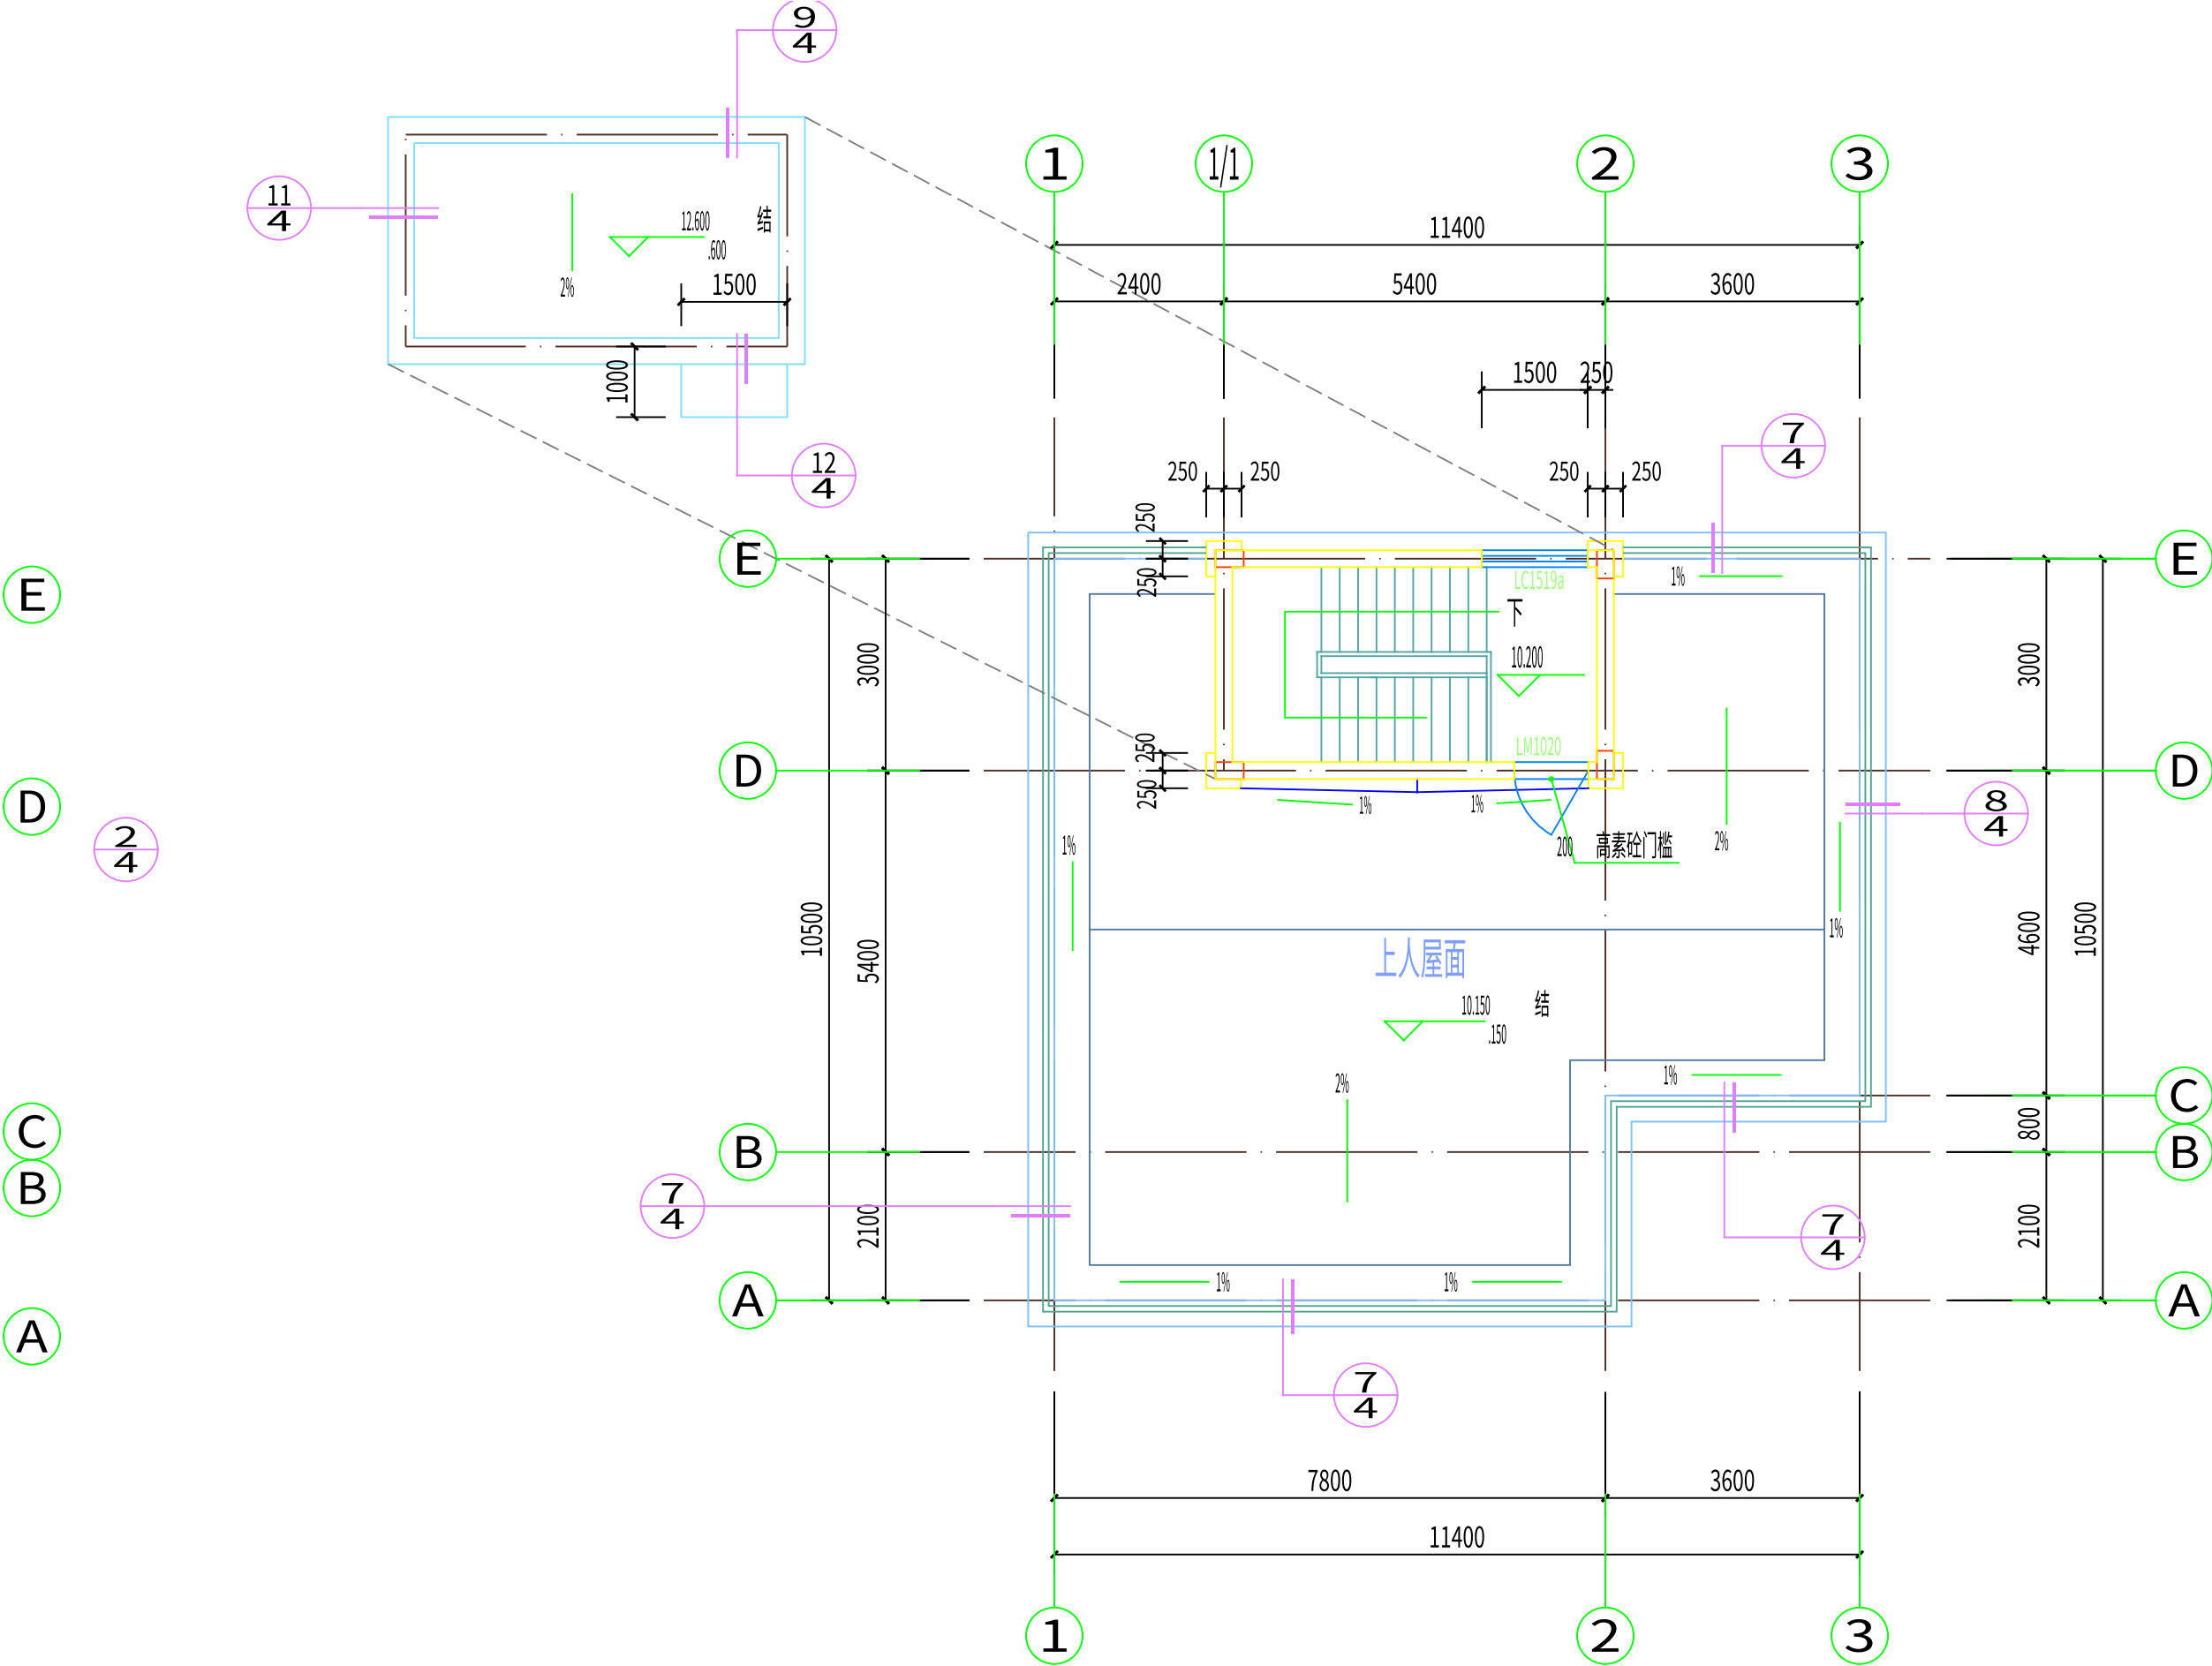


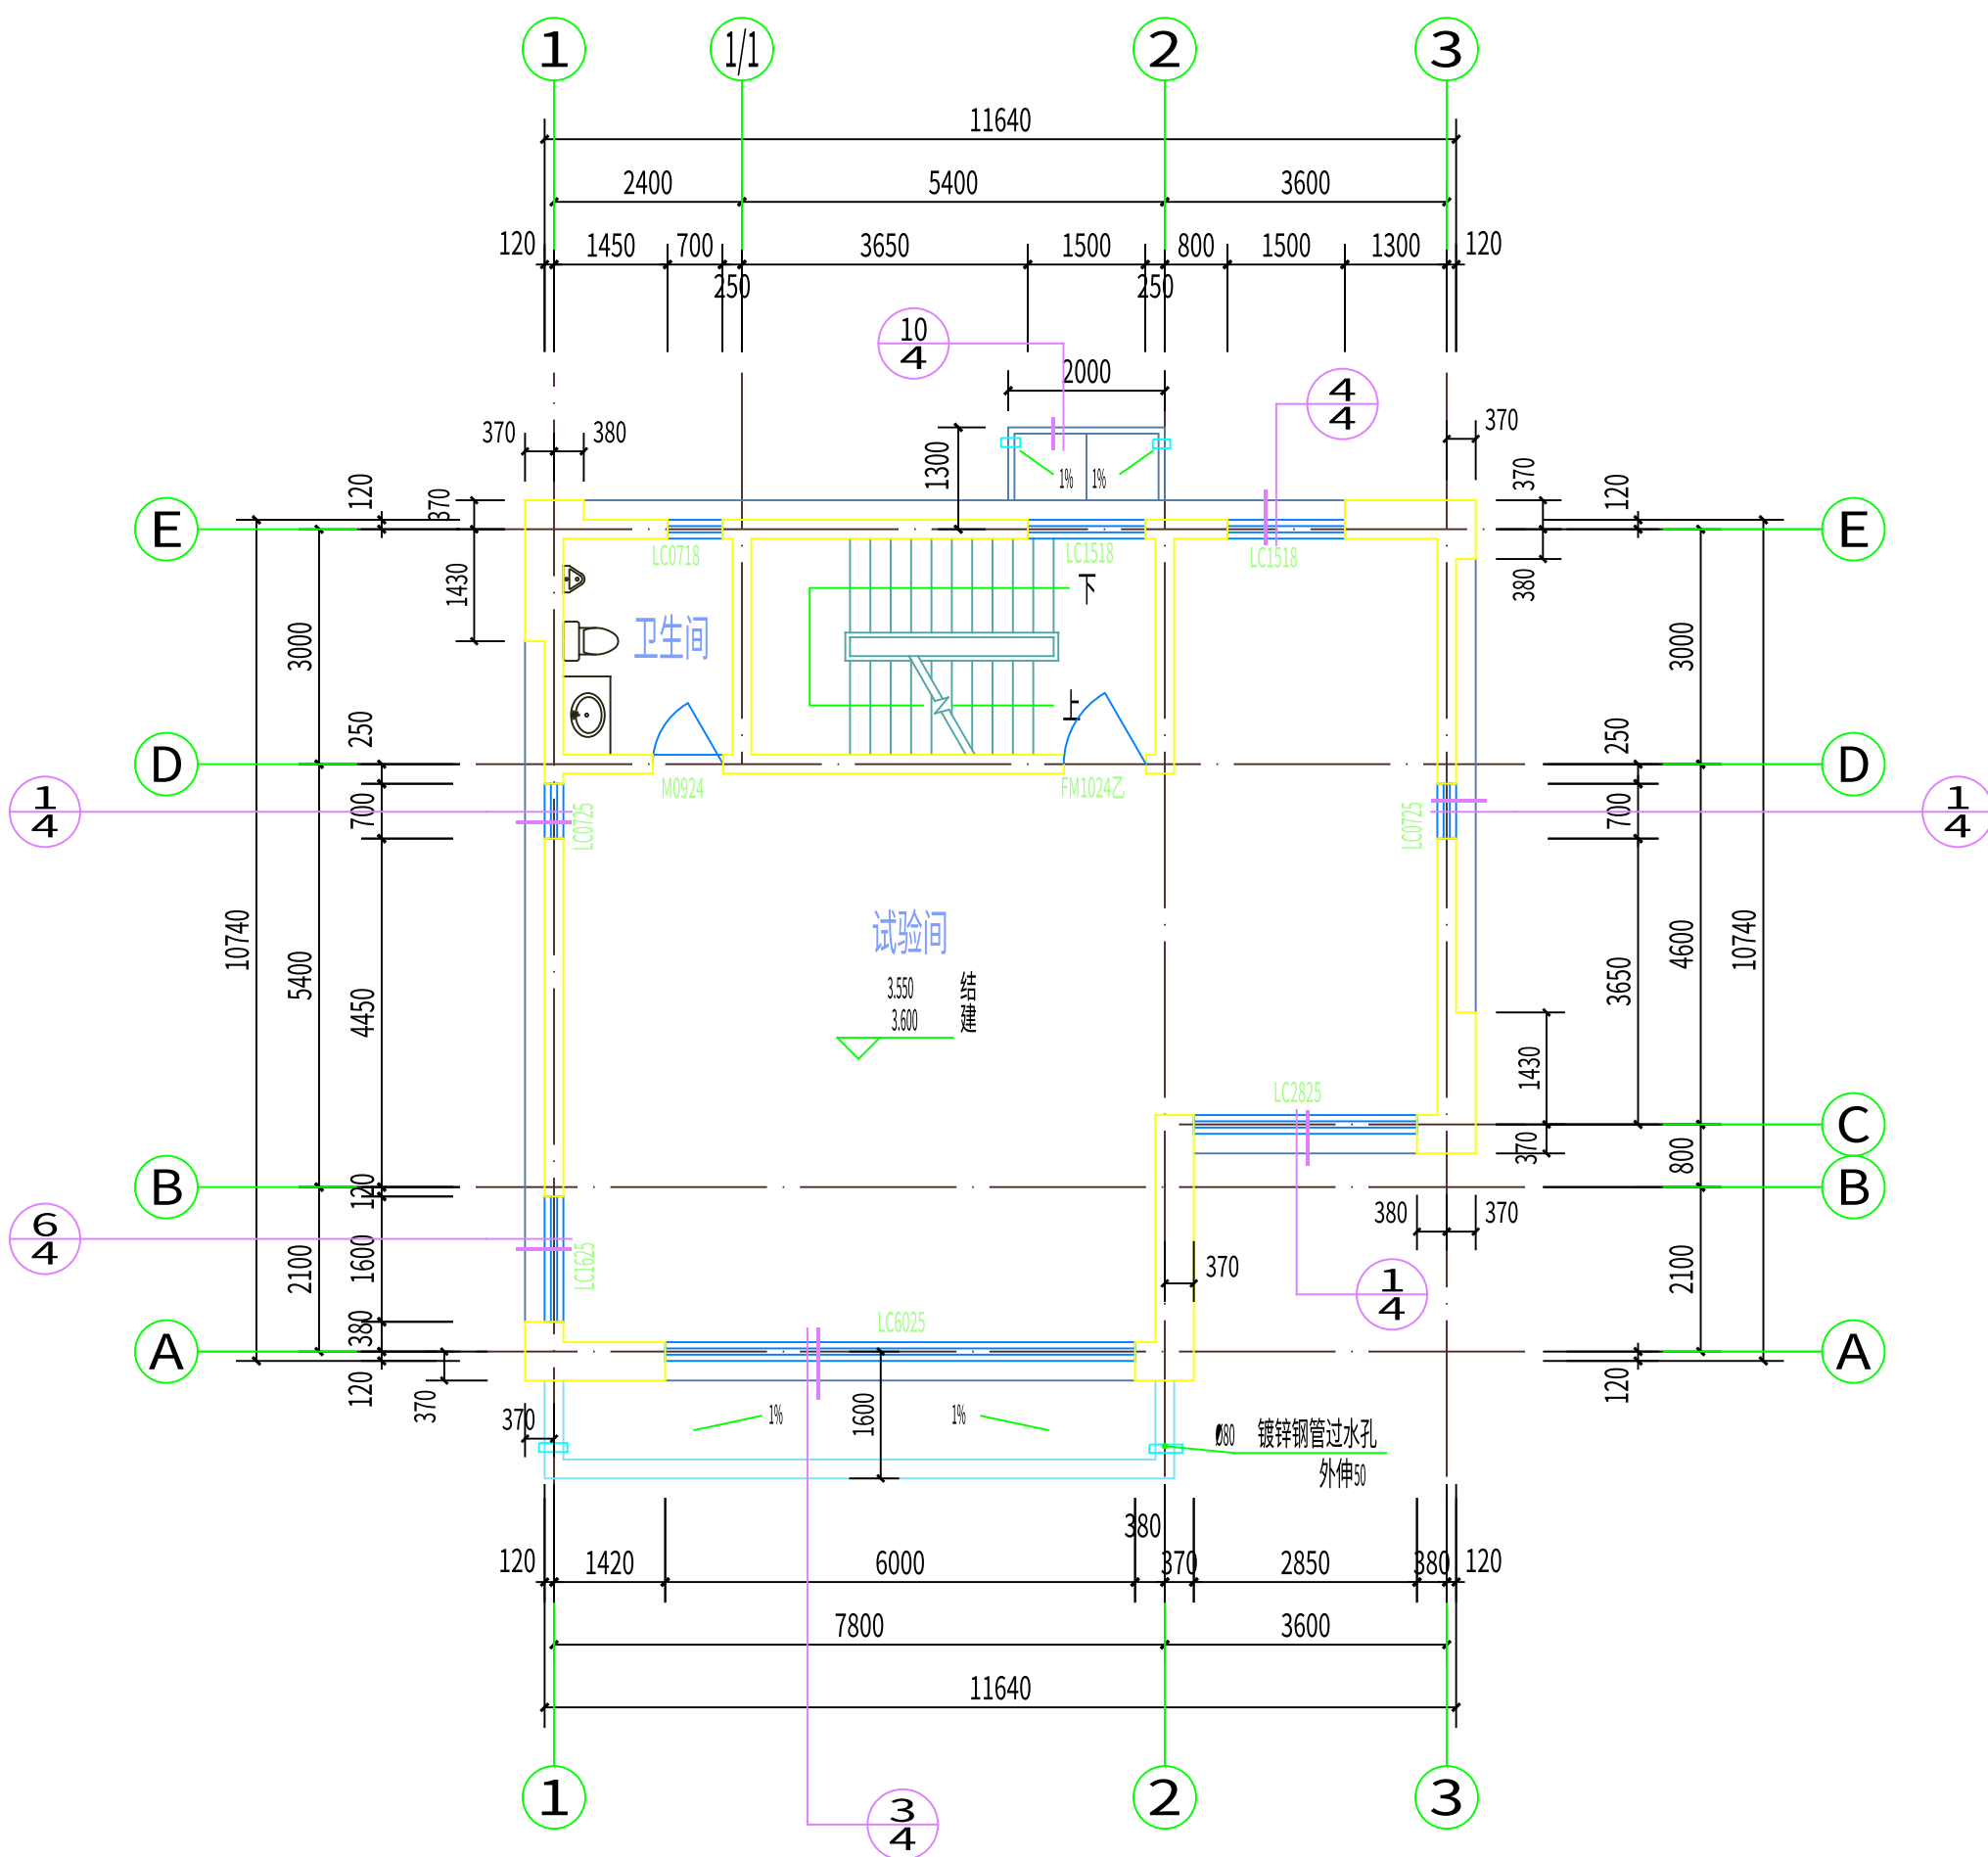

屋顶平面图


1:100

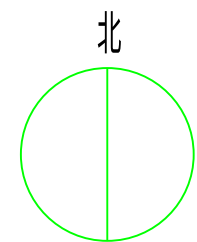

二层平面图


1:100

二层面积：114.6平方米,每层人数不超过10人

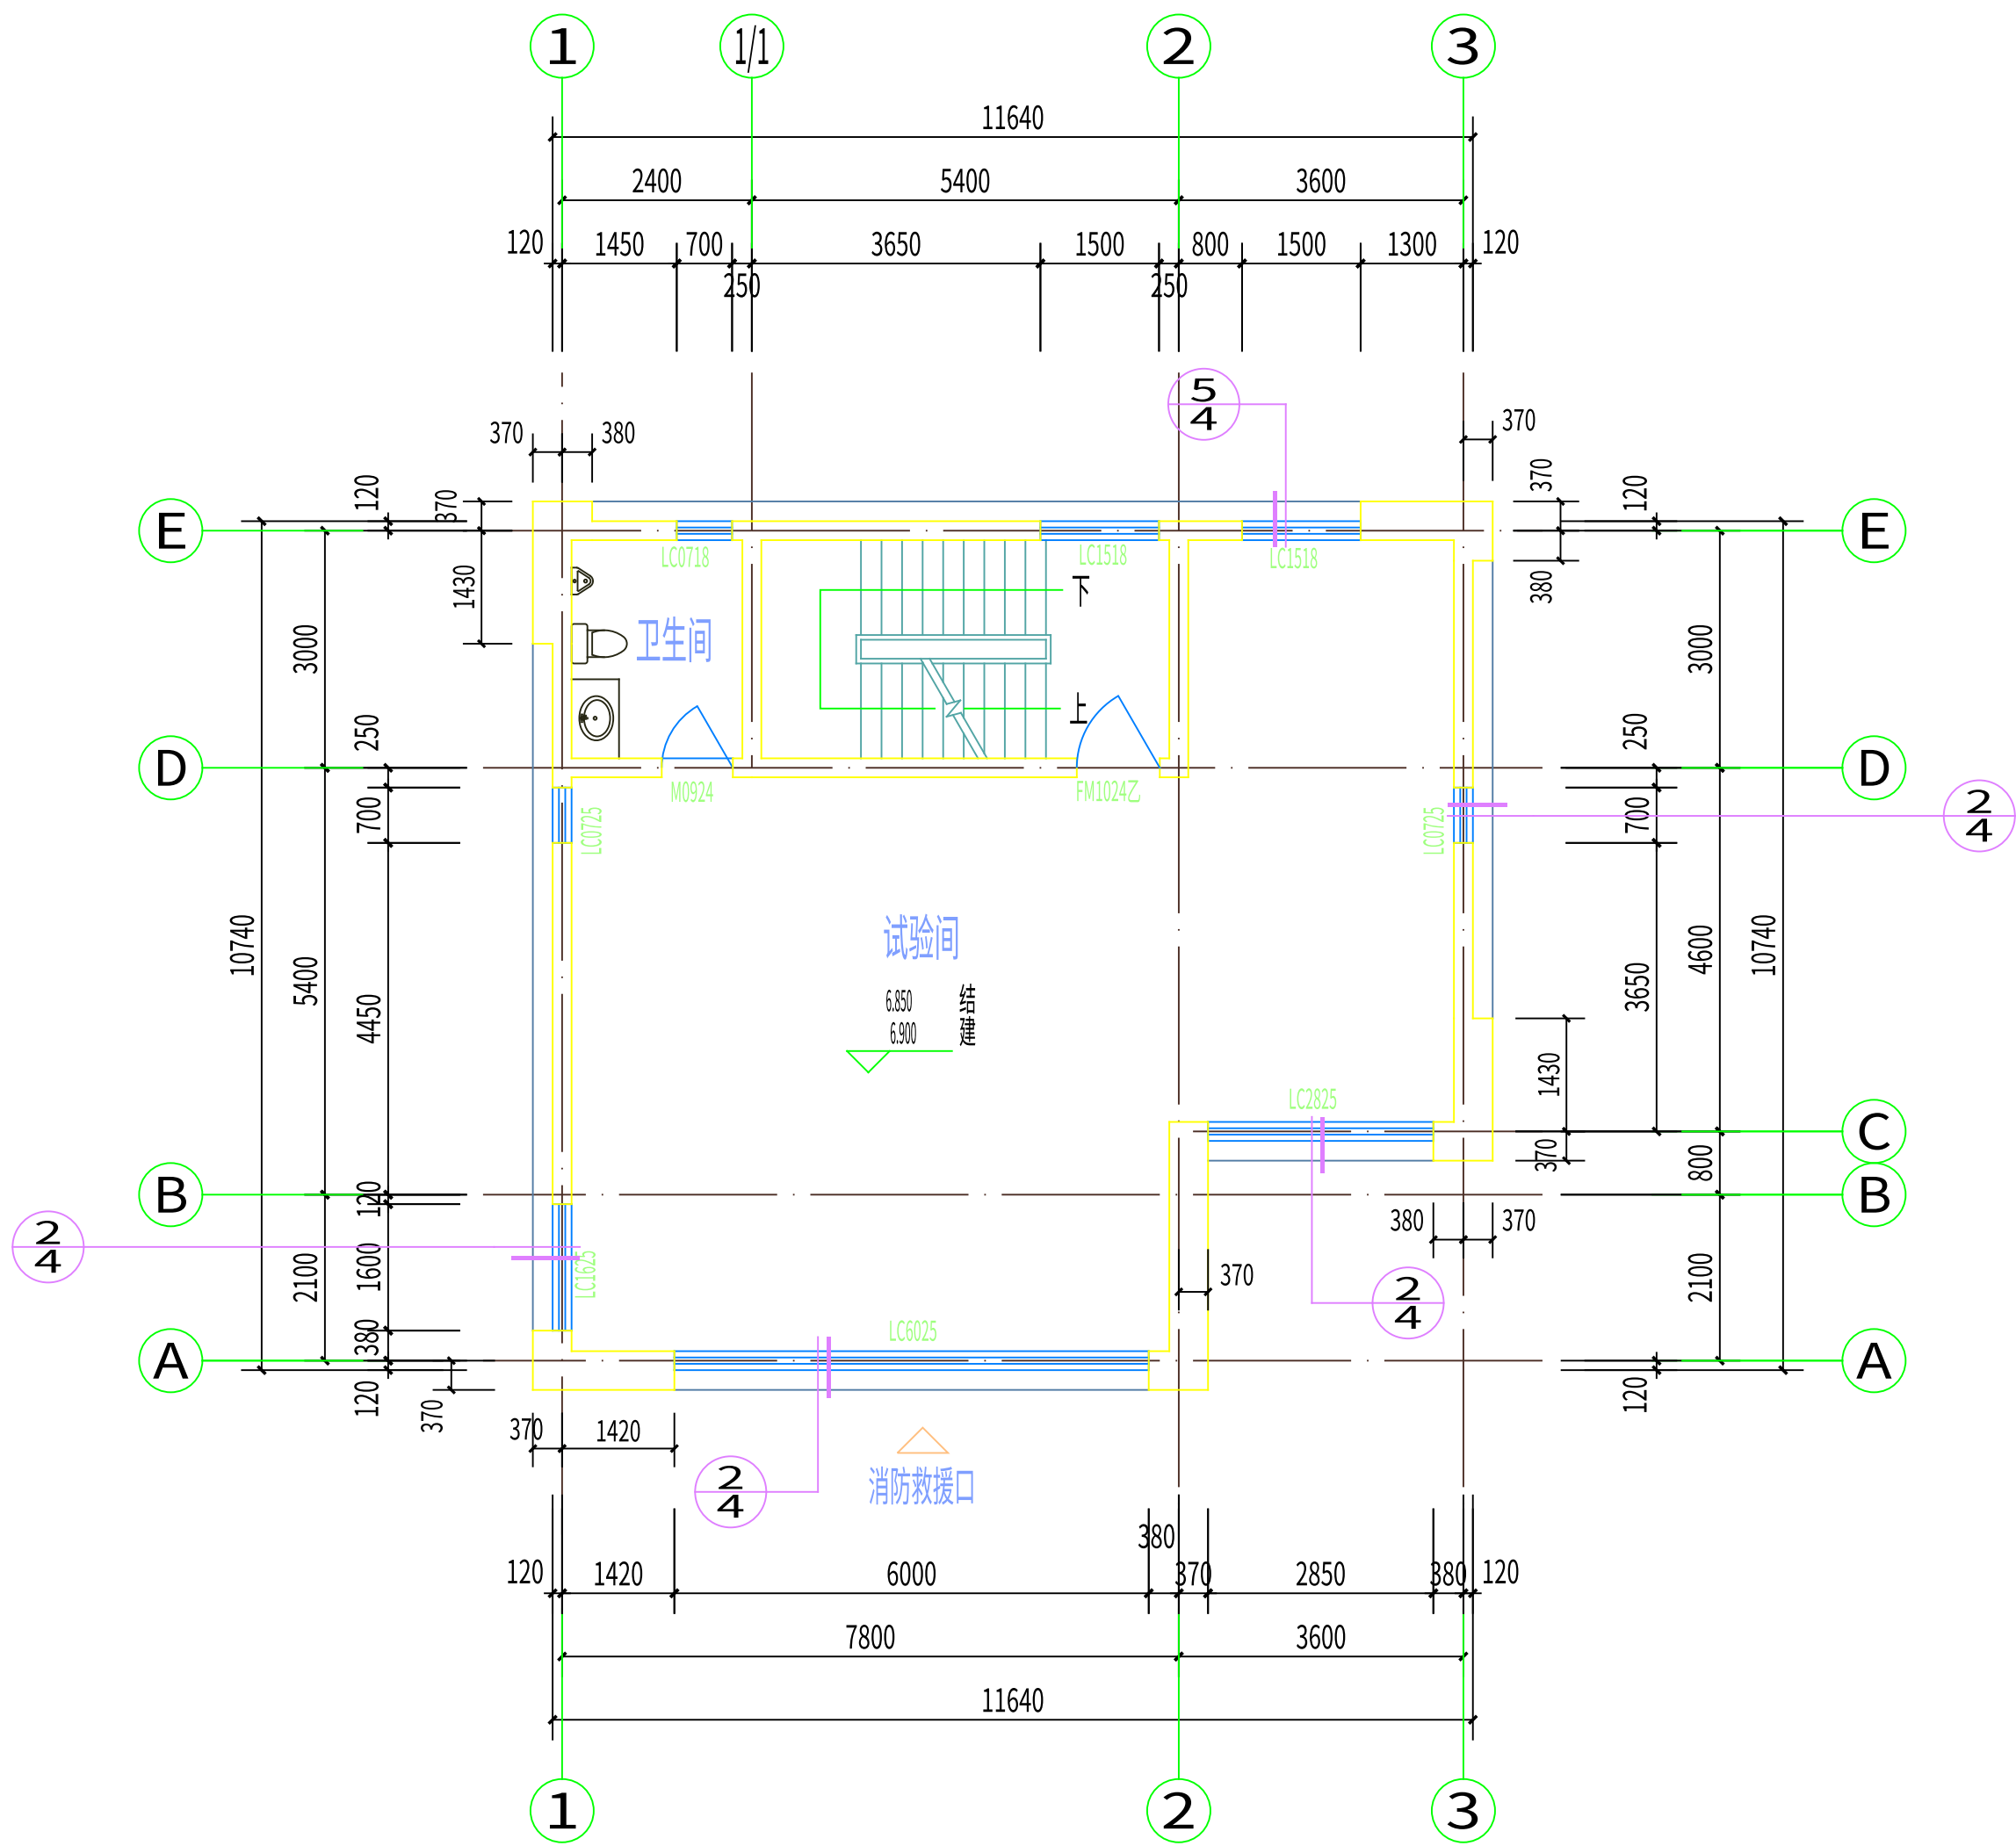

三层平面图 1:100


三层面积：114.6平方米,每层人数不超过10人

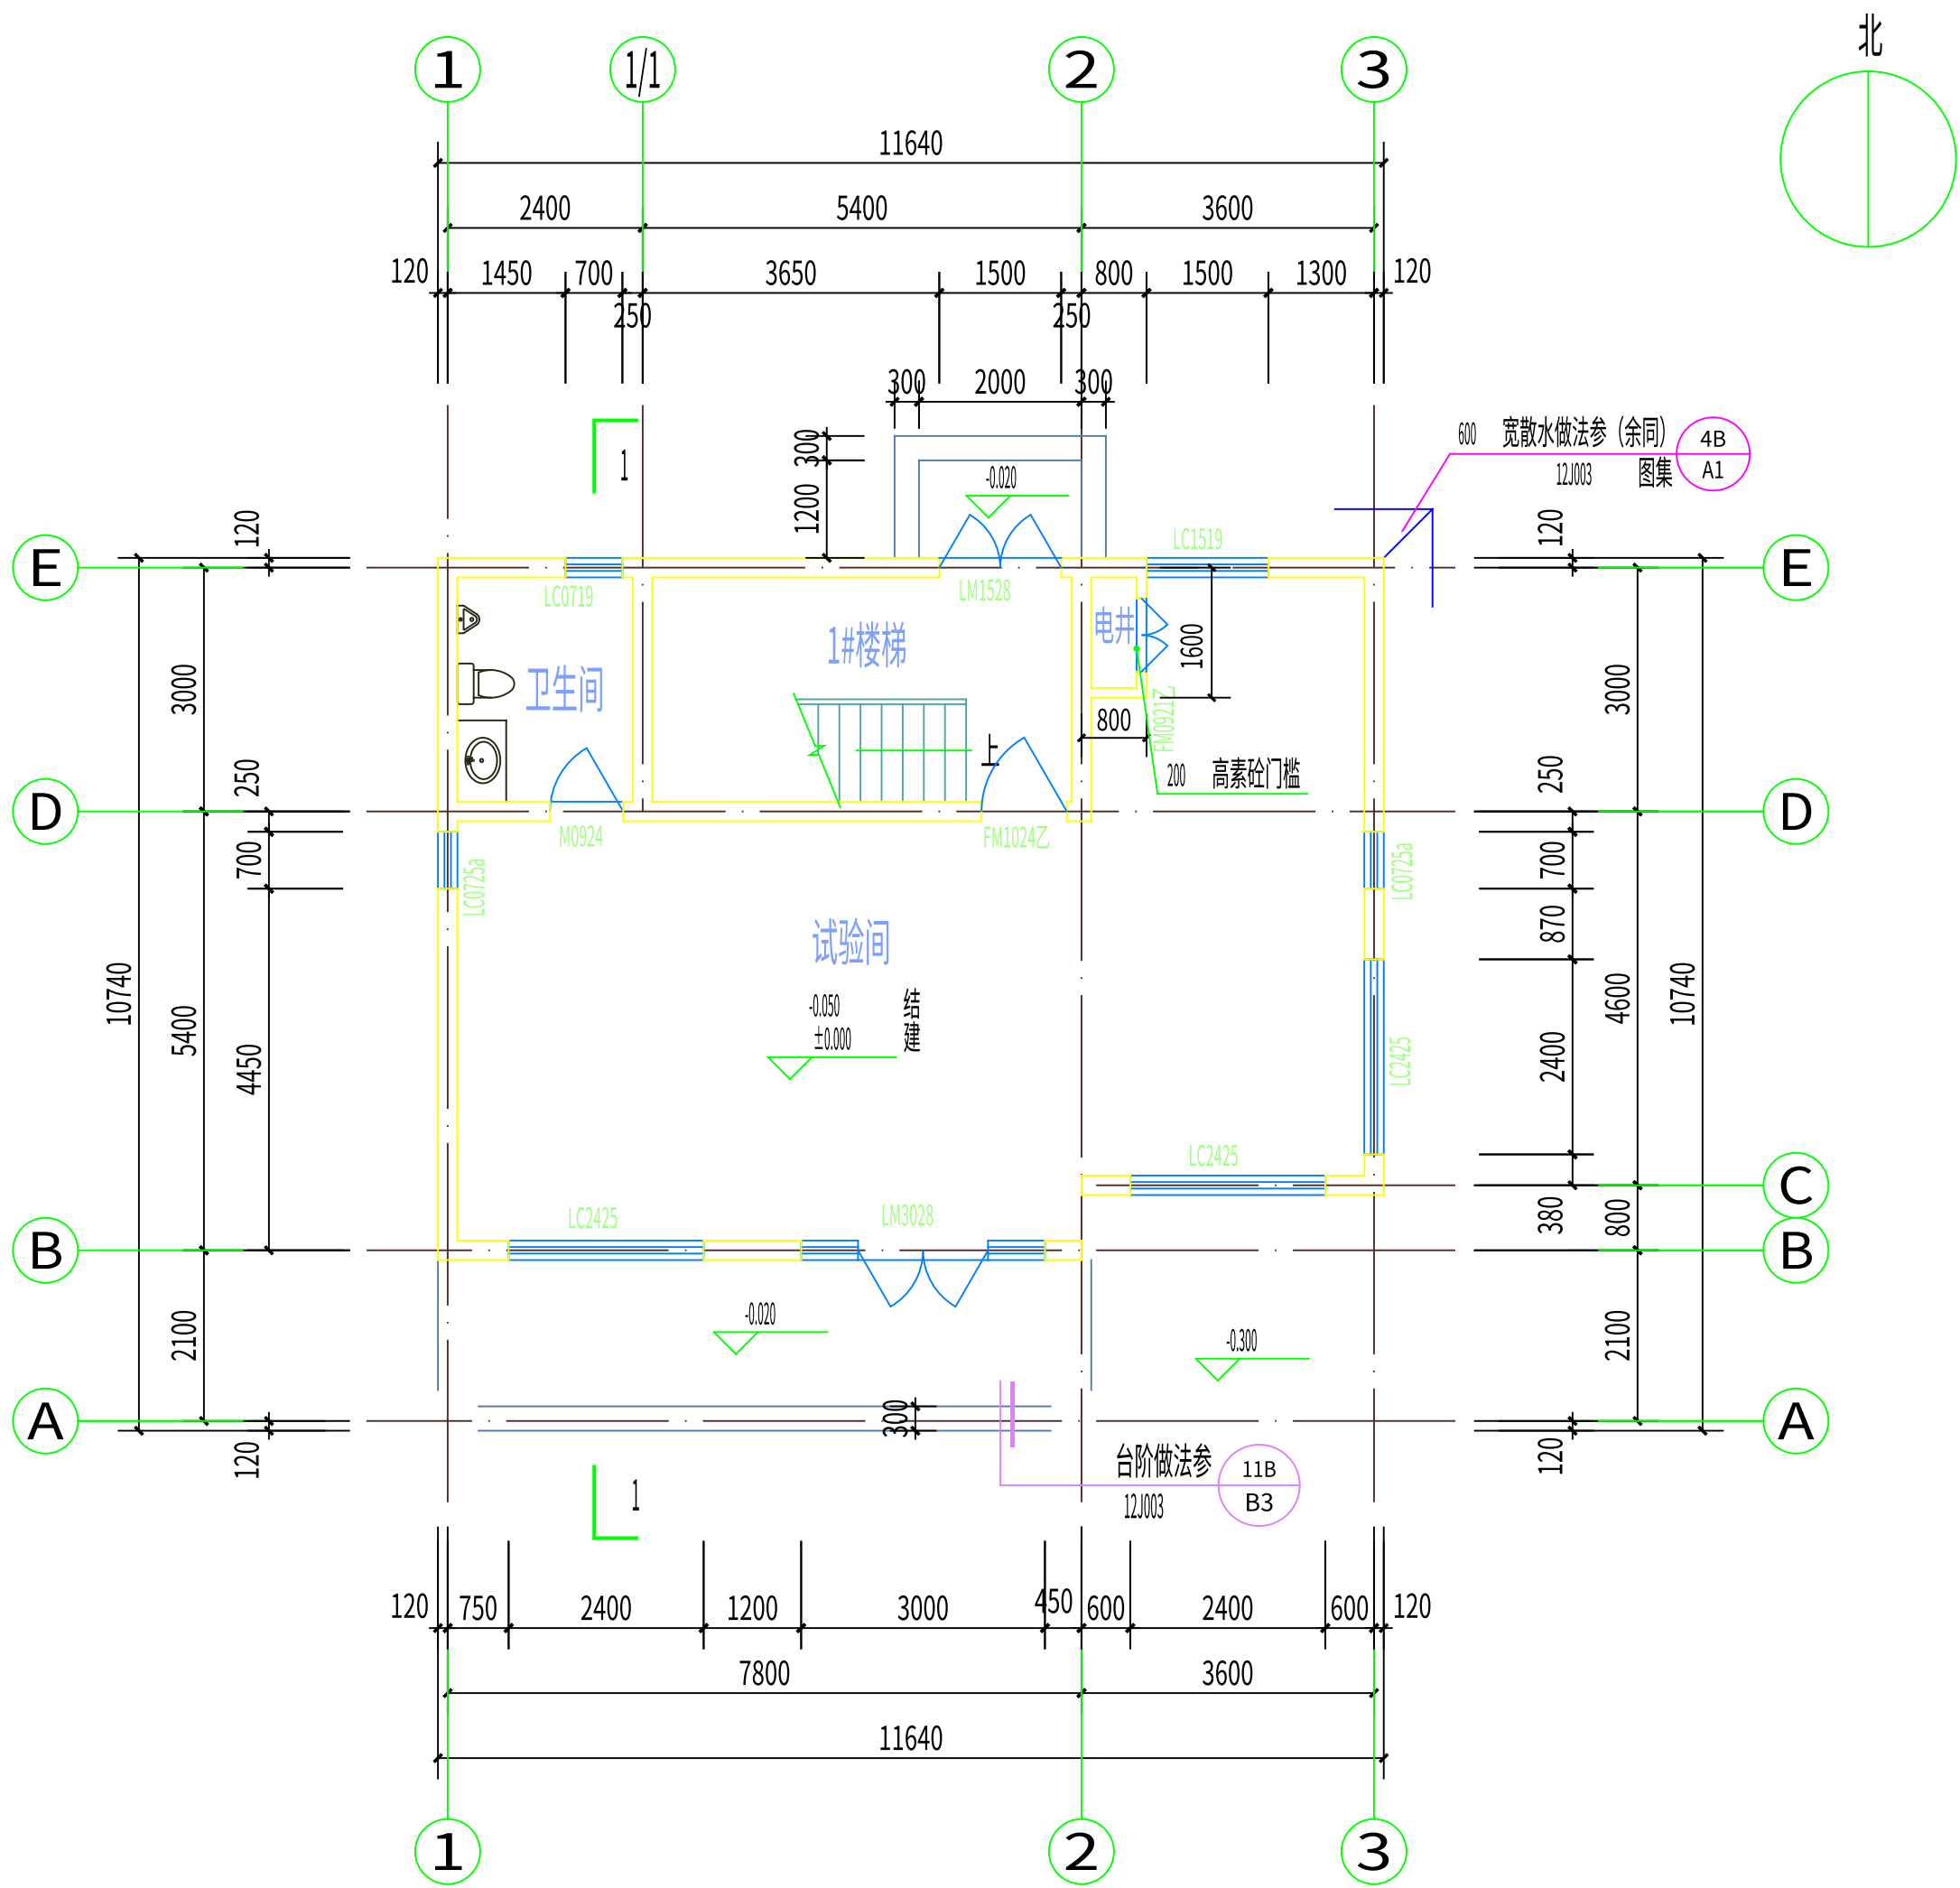



一层平面图 1:100





一层面积：114.6平方米,每层人数不超过10人


暖通	暖通
电气	电气
给排水	给排水
结构	结构
装饰	装饰
建筑	建筑
专业	专业
审核	审核

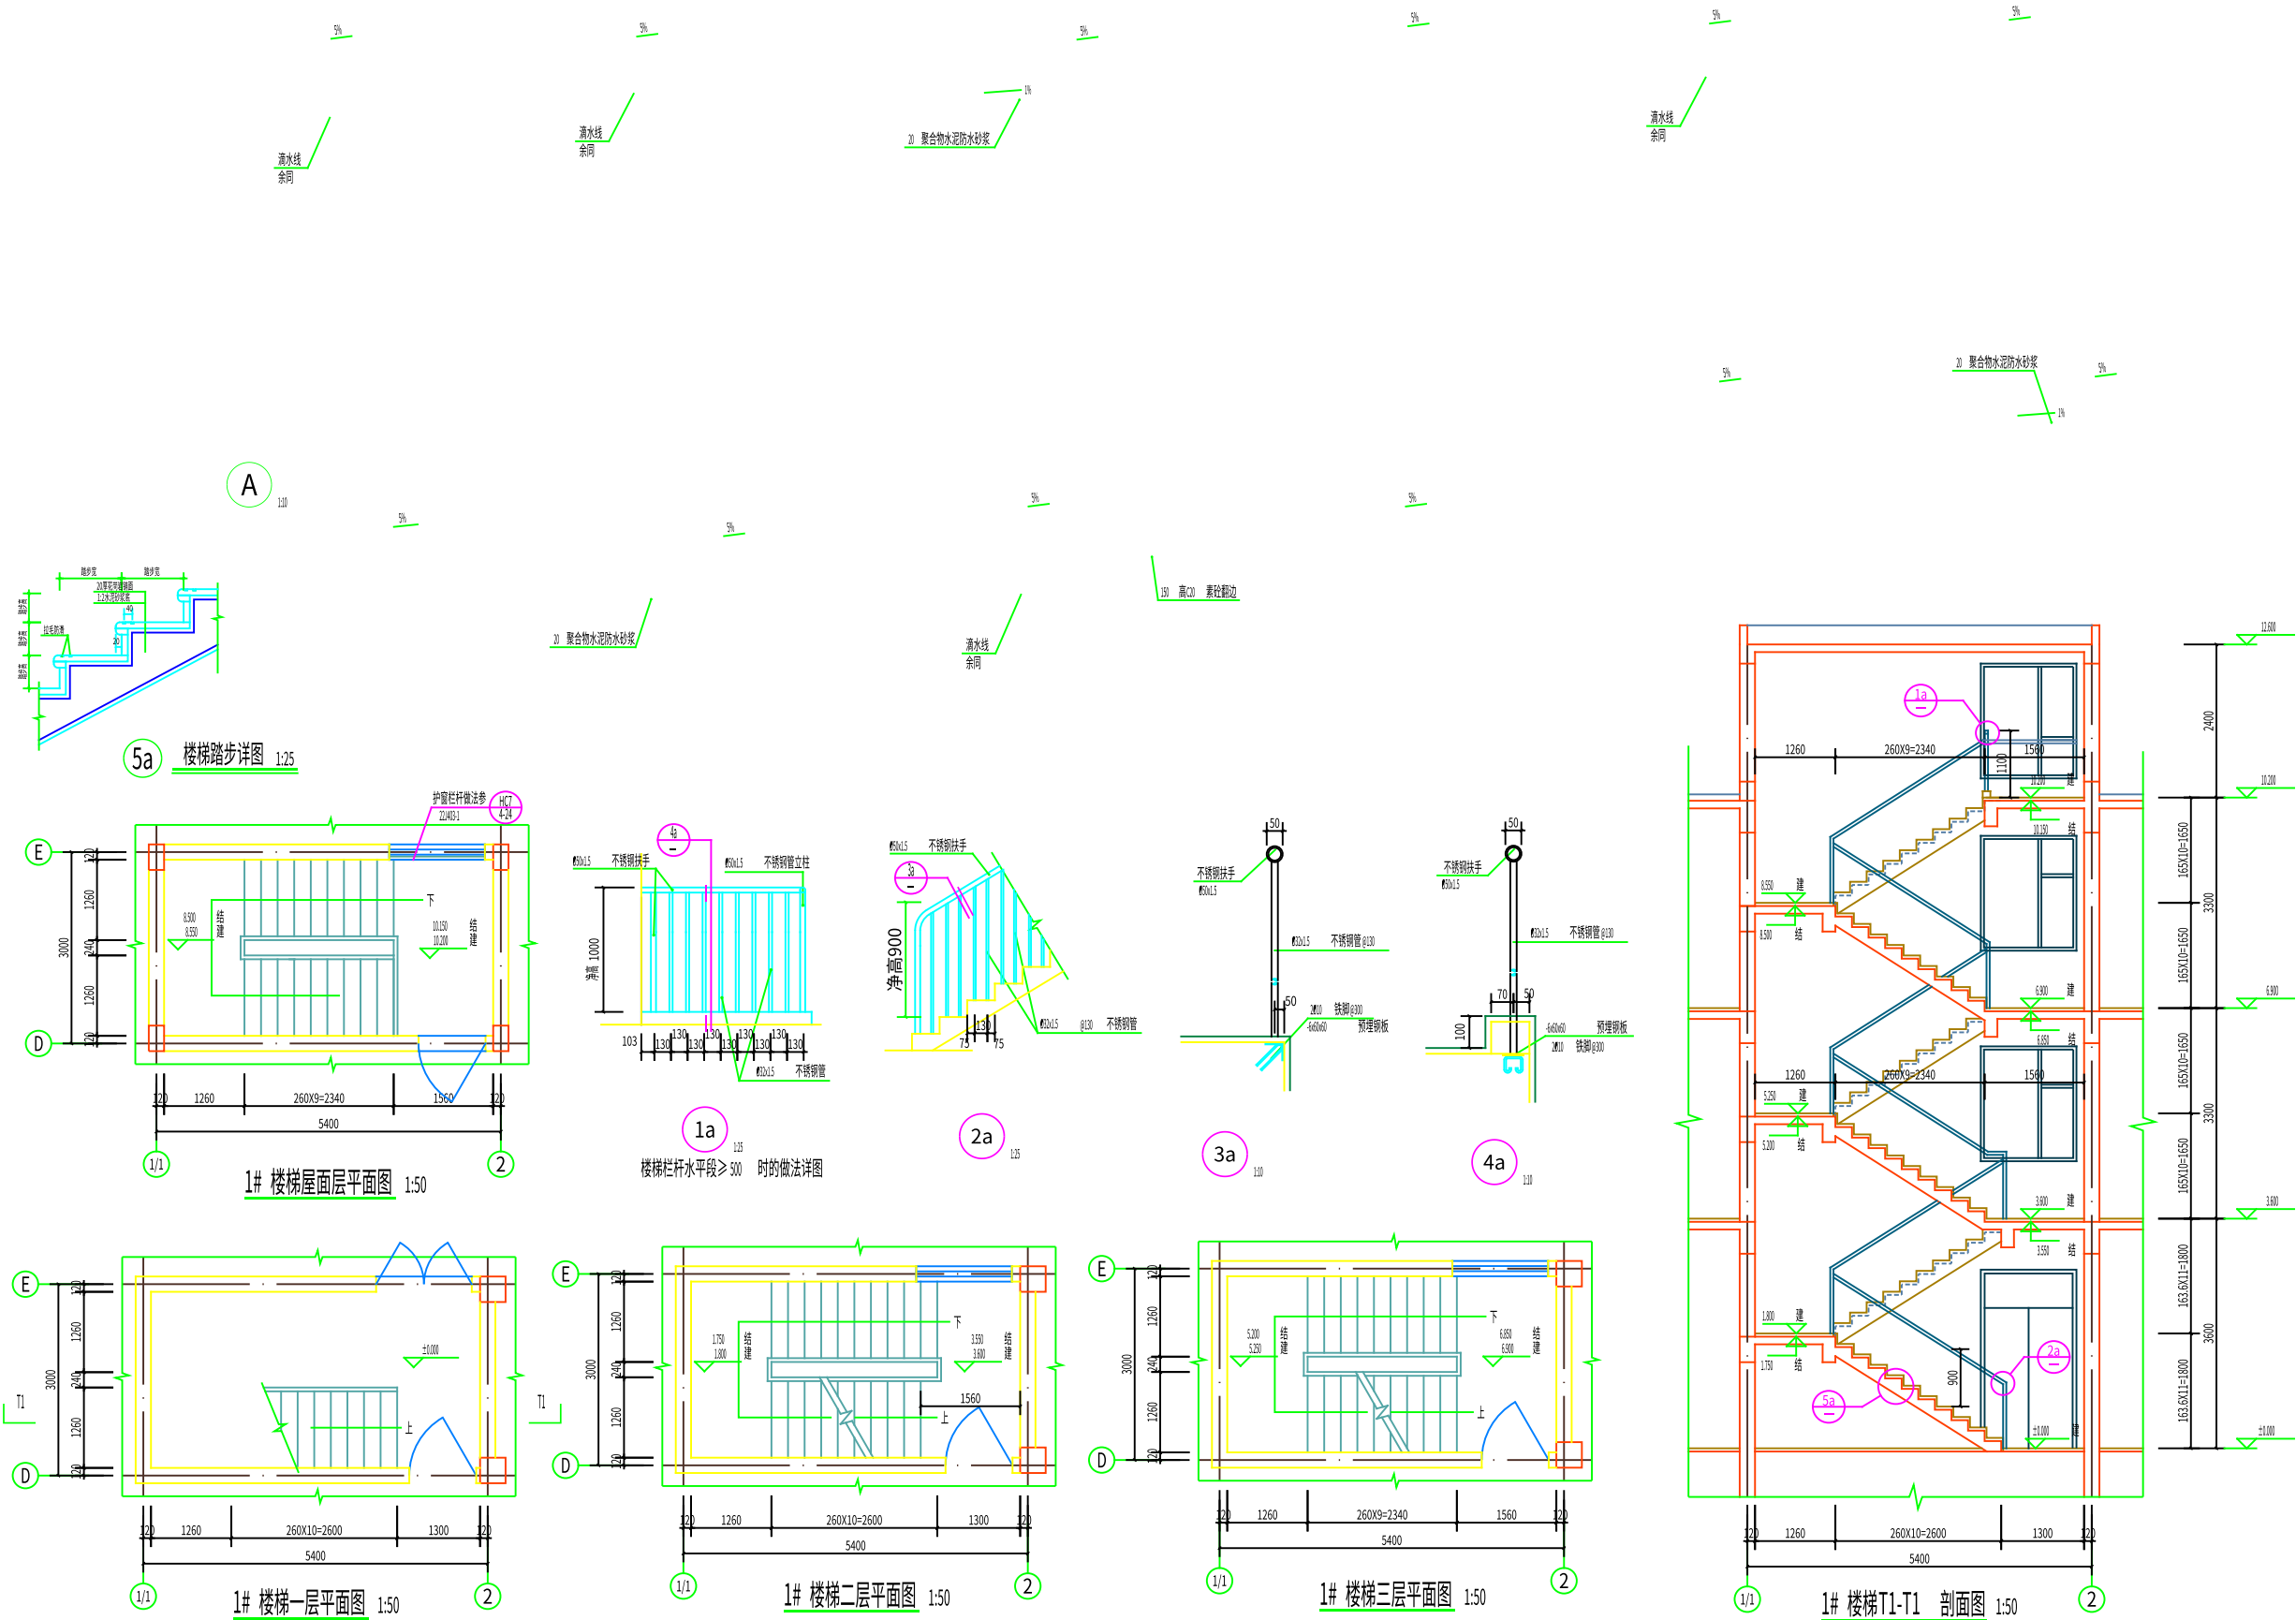


	实 名	签 名	
项目负责人	杨规范		
专业负责人	王朝晖		
设 计 人	吴国峰		
注册（执业）章			
预留章			
出图章			
审图章			
竣工章			
平面图位置			
 蓝绿双城 SHAN CITY SALES CITY 浙江蓝绿双城建筑设计有限公司 ZHEJIANG SHAN CITY SALES CITY ARCHITECTURAL DESIGN CO., LTD. 证书编号: A120000163 法定代表人: 杨规范 中国(杭州)自由贸易试验区工字4号 联系电话: 0571-85000366 传 真: 0571-82755550			
类 别	实 名	签 名	日 期
审 定	李建良		
审 核	王保广		
设计负责	杨规范		
专业负责	王朝晖		
校 对	杨规范		
设 计	吴国峰		
制 图	吴国峰		2023.11
建设单位			
浙江红远科技有限公司			
工程名称			
年产200套精密模具、1000万件汽配与办公用品塑料件建设项目			
子项名称			
试验楼			
制图名称			
1#楼梯详图 节点详图			
工程编号			
6623-005			
图 号			
建施-0004			
修改次数			
浙江蓝绿双城建筑设计有限公司			

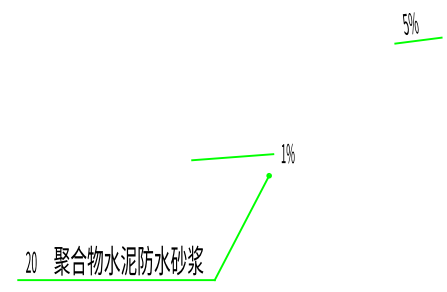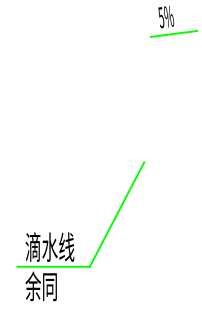

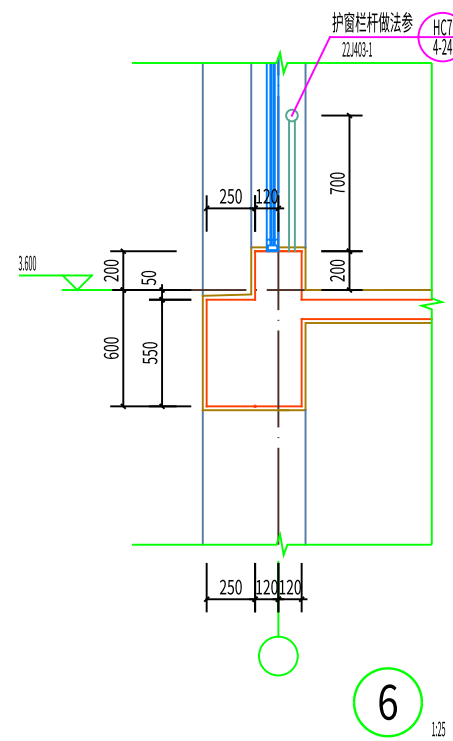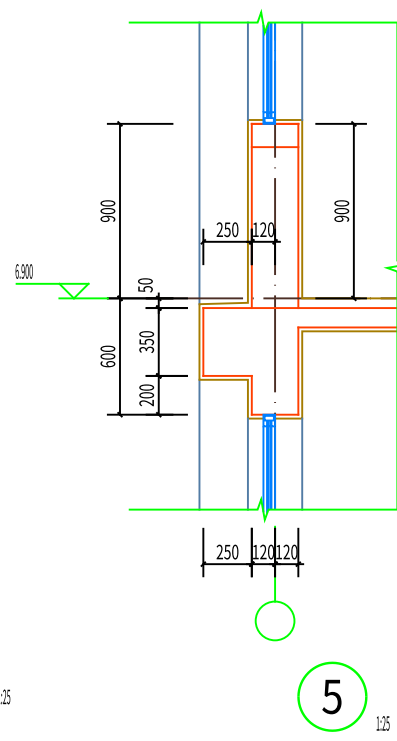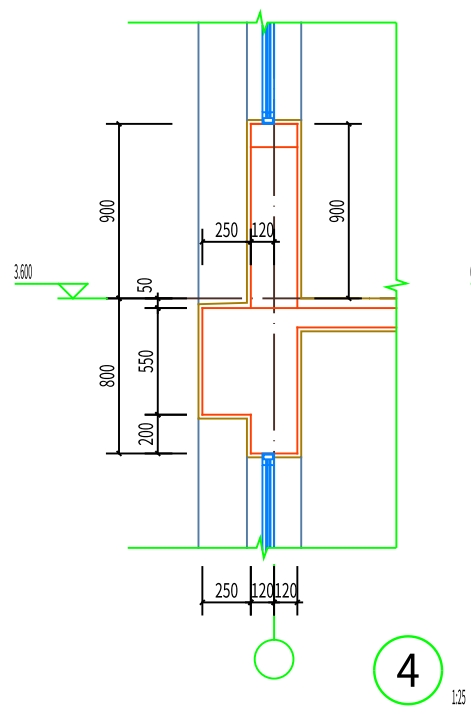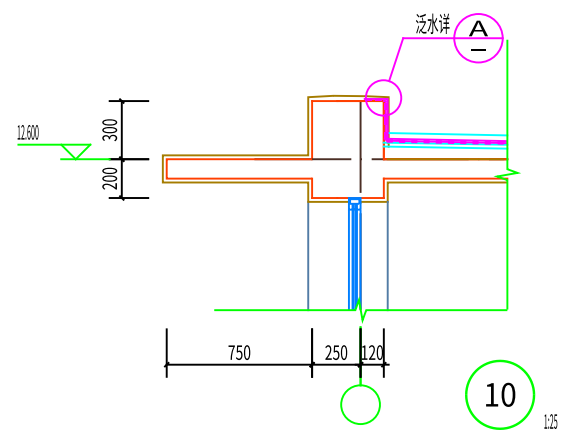

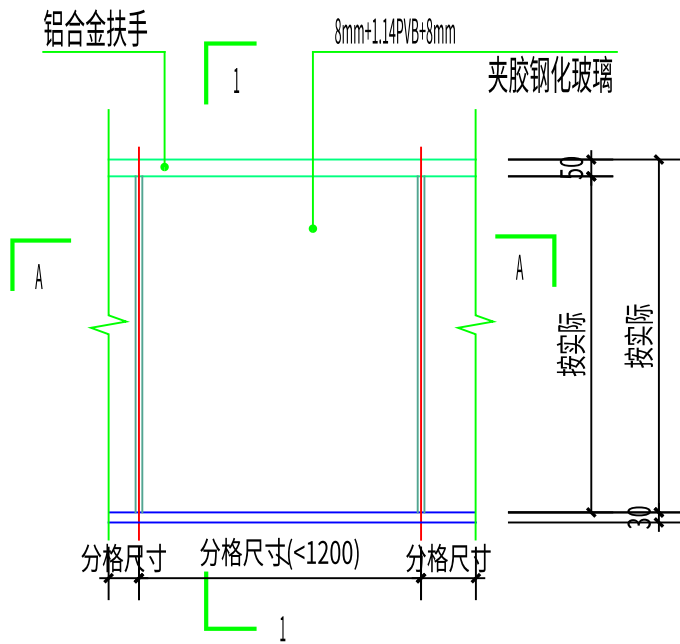


C 玻璃栏板 1:25

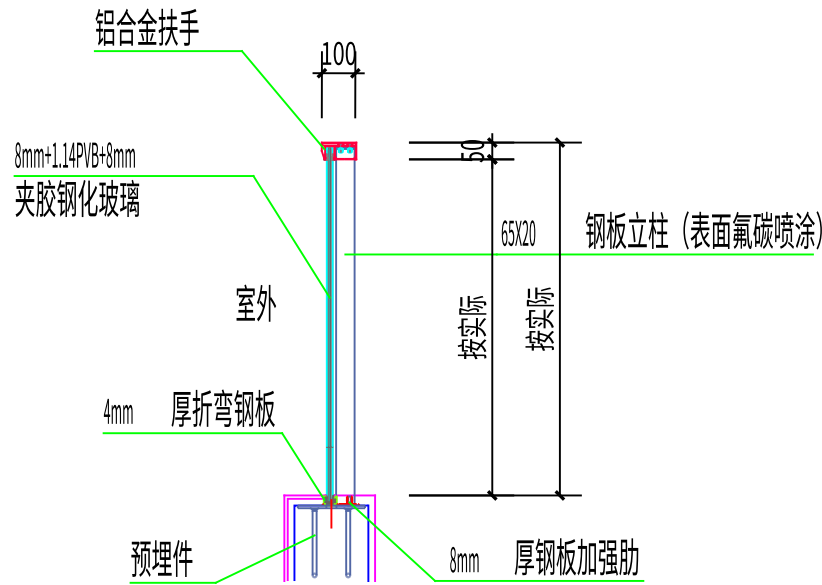

玻璃栏板1-1剖面图 1:25

注：最终实施以厂家提供产品为准，应符合《建筑玻璃应用技术规程》
JGJ113-2015相关检测要求并满足国家要求的水平荷载及安全指数

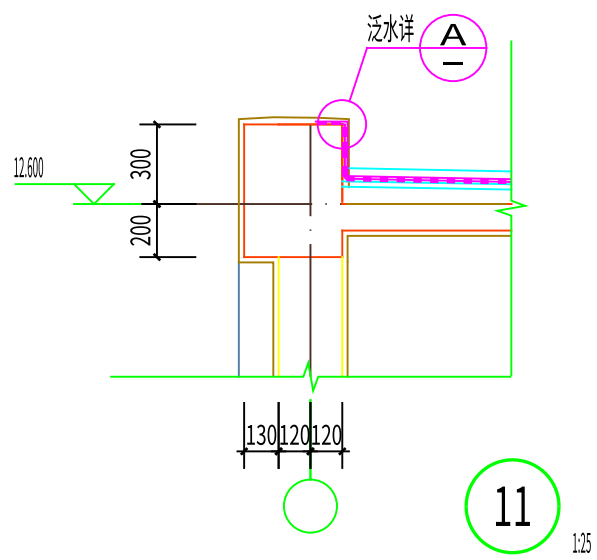

歌咏戦	唱歌
長雨森	長雨
米大	米
種主菜	菜種
	菜種
63 長	63 長
44 第 3 卷	44 第 3 卷

一、工程概况

一	设计依据	
1	《厂房建筑模数协调标准》(GBJ6-86)	
2	《建筑设计防火规范》(GB50016-2014)(2018版)	
3	《民用建筑设计统一标准》(GB 50352-2019)	
4	《浙江省消防技术规范难点问题操作技术指南(2020版)》	
5	浙江省《建筑防水工程技术规程》(DB 33/T 1147-2018)	
6	《屋面工程技术规范》(GB50345-2012)	
7	国家现行的有关建筑设计规范、规程和规定	
二	建筑概况	
1	建筑名称: 年产200套精密模具、1000万件汽配与办公用品塑料件建设项目	
2	本工程相对标高±0.000相当于1985国家高程基准高程 米, 定位坐标见总图	
3	建筑占地面积: 115 平方米	
4	建筑面积:	地上: 368.41 平方米
5	建筑层数:	地上 层
6	建筑高度:	消防高度: 10.50米 规划高度: 10.80米
7	建筑分类:	生产的火灾危险性分类: 丙类 (非人员密集型车间)
8	建筑耐火等级:	地上二级
9	建筑结构类型:	框架结构
10	抗震设防烈度:	7 度
11	屋面防水等级:	一级
12	建筑设计使用年限:	50 年
13	工业建筑节能设计类别: 二类 (本工程为产品试验车间, 不需要设置空调节能, 通过自然通风设计, 降低通风能耗, 满足《工业建筑节能设计统一标准》GB51245-2017的要求)	

二、消防设计


根据建设单位提供的生产工艺流程,本工程为产品制造试验车间,生产的火灾危险性为丙类,进行消防设计。本工程耐火等级为二级。

- 1、本工程整栋楼作为一个防火分区。防火分区面积满足规范要求。
- 2、安全疏散：根据《建筑设计防火规范》3.7.2条要求，本栋楼防火分区设置1个安全出口，疏散距离满足规范要求。
- 3、安全疏散距离：平面中任意一点至安全疏散口的距离均小于40米，符合防火规范要求。
- 4、防火间距：本工程与相邻建筑间满足防火间距要求。
- 5、消防救援：本工程在消防救援场地外墙处设置灭火救援口，救援口净宽、净高不应小于1000，离地不宜大于1200，玻璃易于破碎，并在室外设置识别标志。
- 6、防火材料：本工程±0.000以上的墙体均采用烧结页岩多孔砖，梁板、柱、楼梯均为钢筋混凝土现浇，保护层厚度满足耐火等级二级要求，开向封闭楼梯间的门均为乙级防火门。

三、图例

-  钢筋混凝土柱  120厚和240厚墙体 (烧结页岩多孔砖)
 配电箱
 雨水管
 地漏  灭火器
 自救式消防软管卷盘箱
 甲型单栓室内消火栓

1. 图中未注门窗垛宽均为0或120
2. 电表箱、配电箱、消火栓位置仅供参考, 安装高度及大小详相关设备施工图;
3. 公共管井防火门标注尺寸详见平面图, 门下做200高C20混凝土翻边;
4. 除特别注明外, 卫生间地面排水坡度均为1%~4%, 坡向地漏, 建筑完成面标高H+0.020;

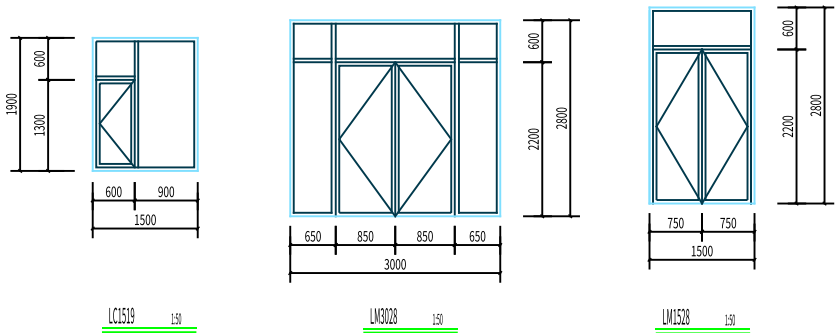


门窗表

类别	门窗编号	门窗名称	洞口尺寸 (mm) (宽/高)	门窗数量				图 集	图 号	备注
				一层	二层	三层	合 计			
门	HM001	铝合金平开门	3000X2300	1			1			
	HM002	铝合金平开门	3500X2300	1			1			
	HM003	铝合金平开门	3000X2000			1	1			
	HM004	夹板木门	900X1400	1	1	1	3			
	HM005Z	乙级木质防火门	1050X2400	1	1	1	3	12J609	参M1FM3-1024 (乙)	
	HM006Z	乙级木质防火门	900X2100				1	12J609	参M1FM-1521 (乙)	
窗	LC001Z	铝合金平开窗	2400X2500	3			3			
	LC002Z	铝合金平开窗	700X2500	2			2			
	LC003Z	铝合金平开窗	700X1500		2	2	4			
	LC004Z	铝合金平开窗	700X1500	1			1			
	LC005Z	铝合金平开窗	3500X1900	1			1			
	LC006Z	铝合金平开窗	6000X2500		1	1	2			
	LC007Z	铝合金平开窗	2850X2500		1	1	2			
	LC008Z	铝合金固定窗	3600X2500		1	1	2			
	LC009Z	铝合金平开窗	800X1300		1	1	2			
	LC010Z	铝合金平开窗	3500X1800		2	2	4			
	LC011Z	铝合金平开窗	3500X1900		1	1	1			


注:

- 本工程须按照洞口门窗数量及洞口尺寸, 以实际情况为准, 生产施工前, 厂家对洞口测量进行实测, 门窗立面详图仅供参考, 门窗详表中所列尺寸均为洞口尺寸, 门窗立面详图仅供参考, 最终以专业单位深化设计确定尺寸为准。门窗的实际尺寸根据外墙饰面材料厚度及结构材料厚度进行核算, 商家专业设计单位提供
- 本工程采用金属型材密封铝中空玻璃(设计时要求洛氏硬度必须< 14HV), 中空玻璃为 6mm 中空钢化 12mm 钢化, 面积为 1.13 平方米的玻璃或玻璃块在落地时最终重量小于 45 公斤的落地窗、铝合金门窗必须使用安全玻璃。
- 本设计只给出门窗立面图, 具体构造详图、型材、规格、强度、防风、防水、保温、密封性能均有生产厂家负责设计
- 楼梯间前室门安装时或后安装时净高度应满足增加相关要求
- 仅作为立面示意图中窗玻璃的规格尺寸标注, 按洞口净宽、净高均小于 300mm, 下底距室内地面不宜大于 120mm 的窗台板、窗洞口与墙洞口同宽。
- 防火门、防火卷帘及防火卷帘等均由专业厂家定制, 具体做法遵照 2018 图集。


消防数据口

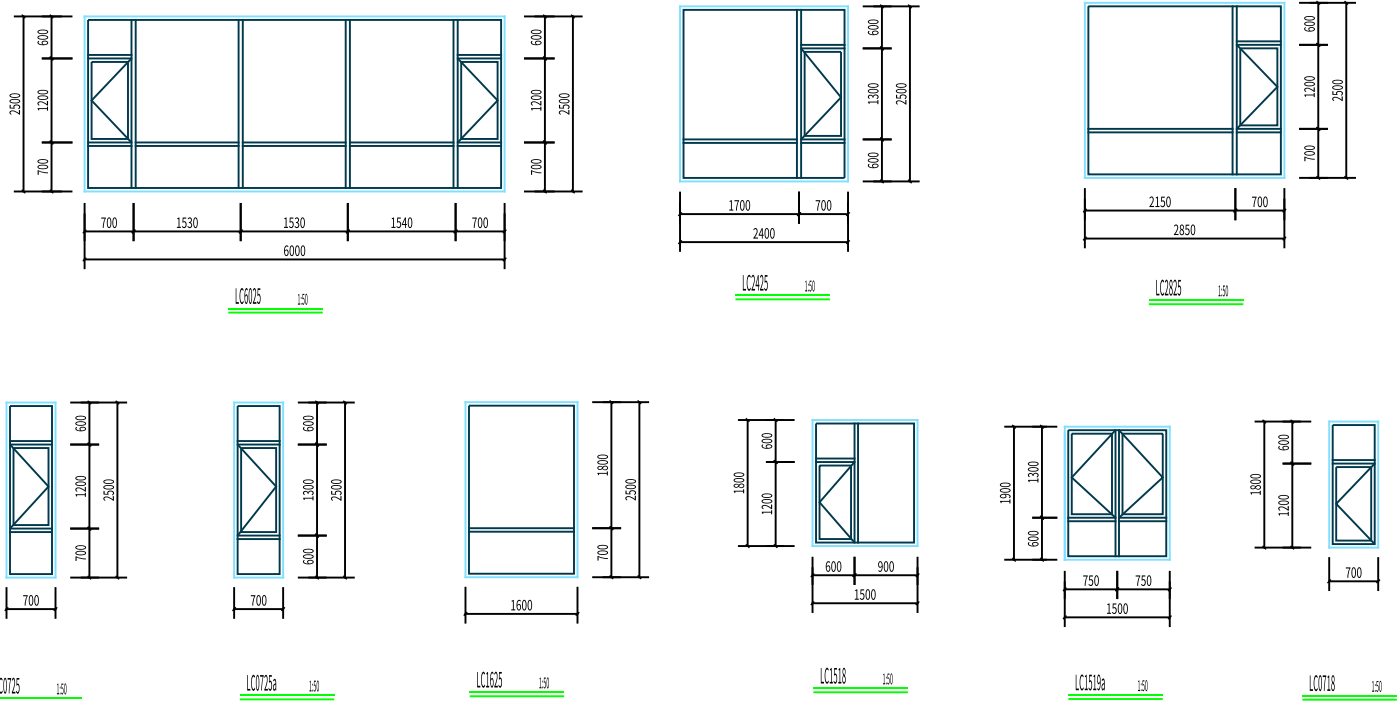


	实 名	签 名	
项目负责人	杨观法		
专业负责人	王朝晖		
设计人	吴国峰		
注册（执业）章			
预留章			
出图章			
审图章			
竣工章			
平断面图章			
 蓝绿双城 zhuangcitydesign.com 浙江蓝绿双城建筑设计有限公司 ZHEJIANG SHANGT CITY SHALE CITY ARCHITECTURAL DESIGN CO.,LTD 证书编号：A133001163 证书等级：建筑 甲级 中国·杭州·钱江世纪城22号大厦 · 设计电话：0571-62703366 传 真：0571-62703399			
类别	实名	签名	日期
审 定	李建良		
审 核	王保广		
总设计师	杨观法		
专业负责	王朝晖		
校 核	杨观法		
设 计	吴国峰		
制 图	吴国峰		2023.11
建设单位 浙江红远科技有限公司			
工程名称 年产200套精密模具、1000万件汽配 与办公用品塑料件建设项自			
子项目名称 试验楼			
图纸名称 工程概况 门窗详图			
工程编号	6623-005		
图号	建施-0001	修改次数	
未加盖竣工图审查章本图无效			

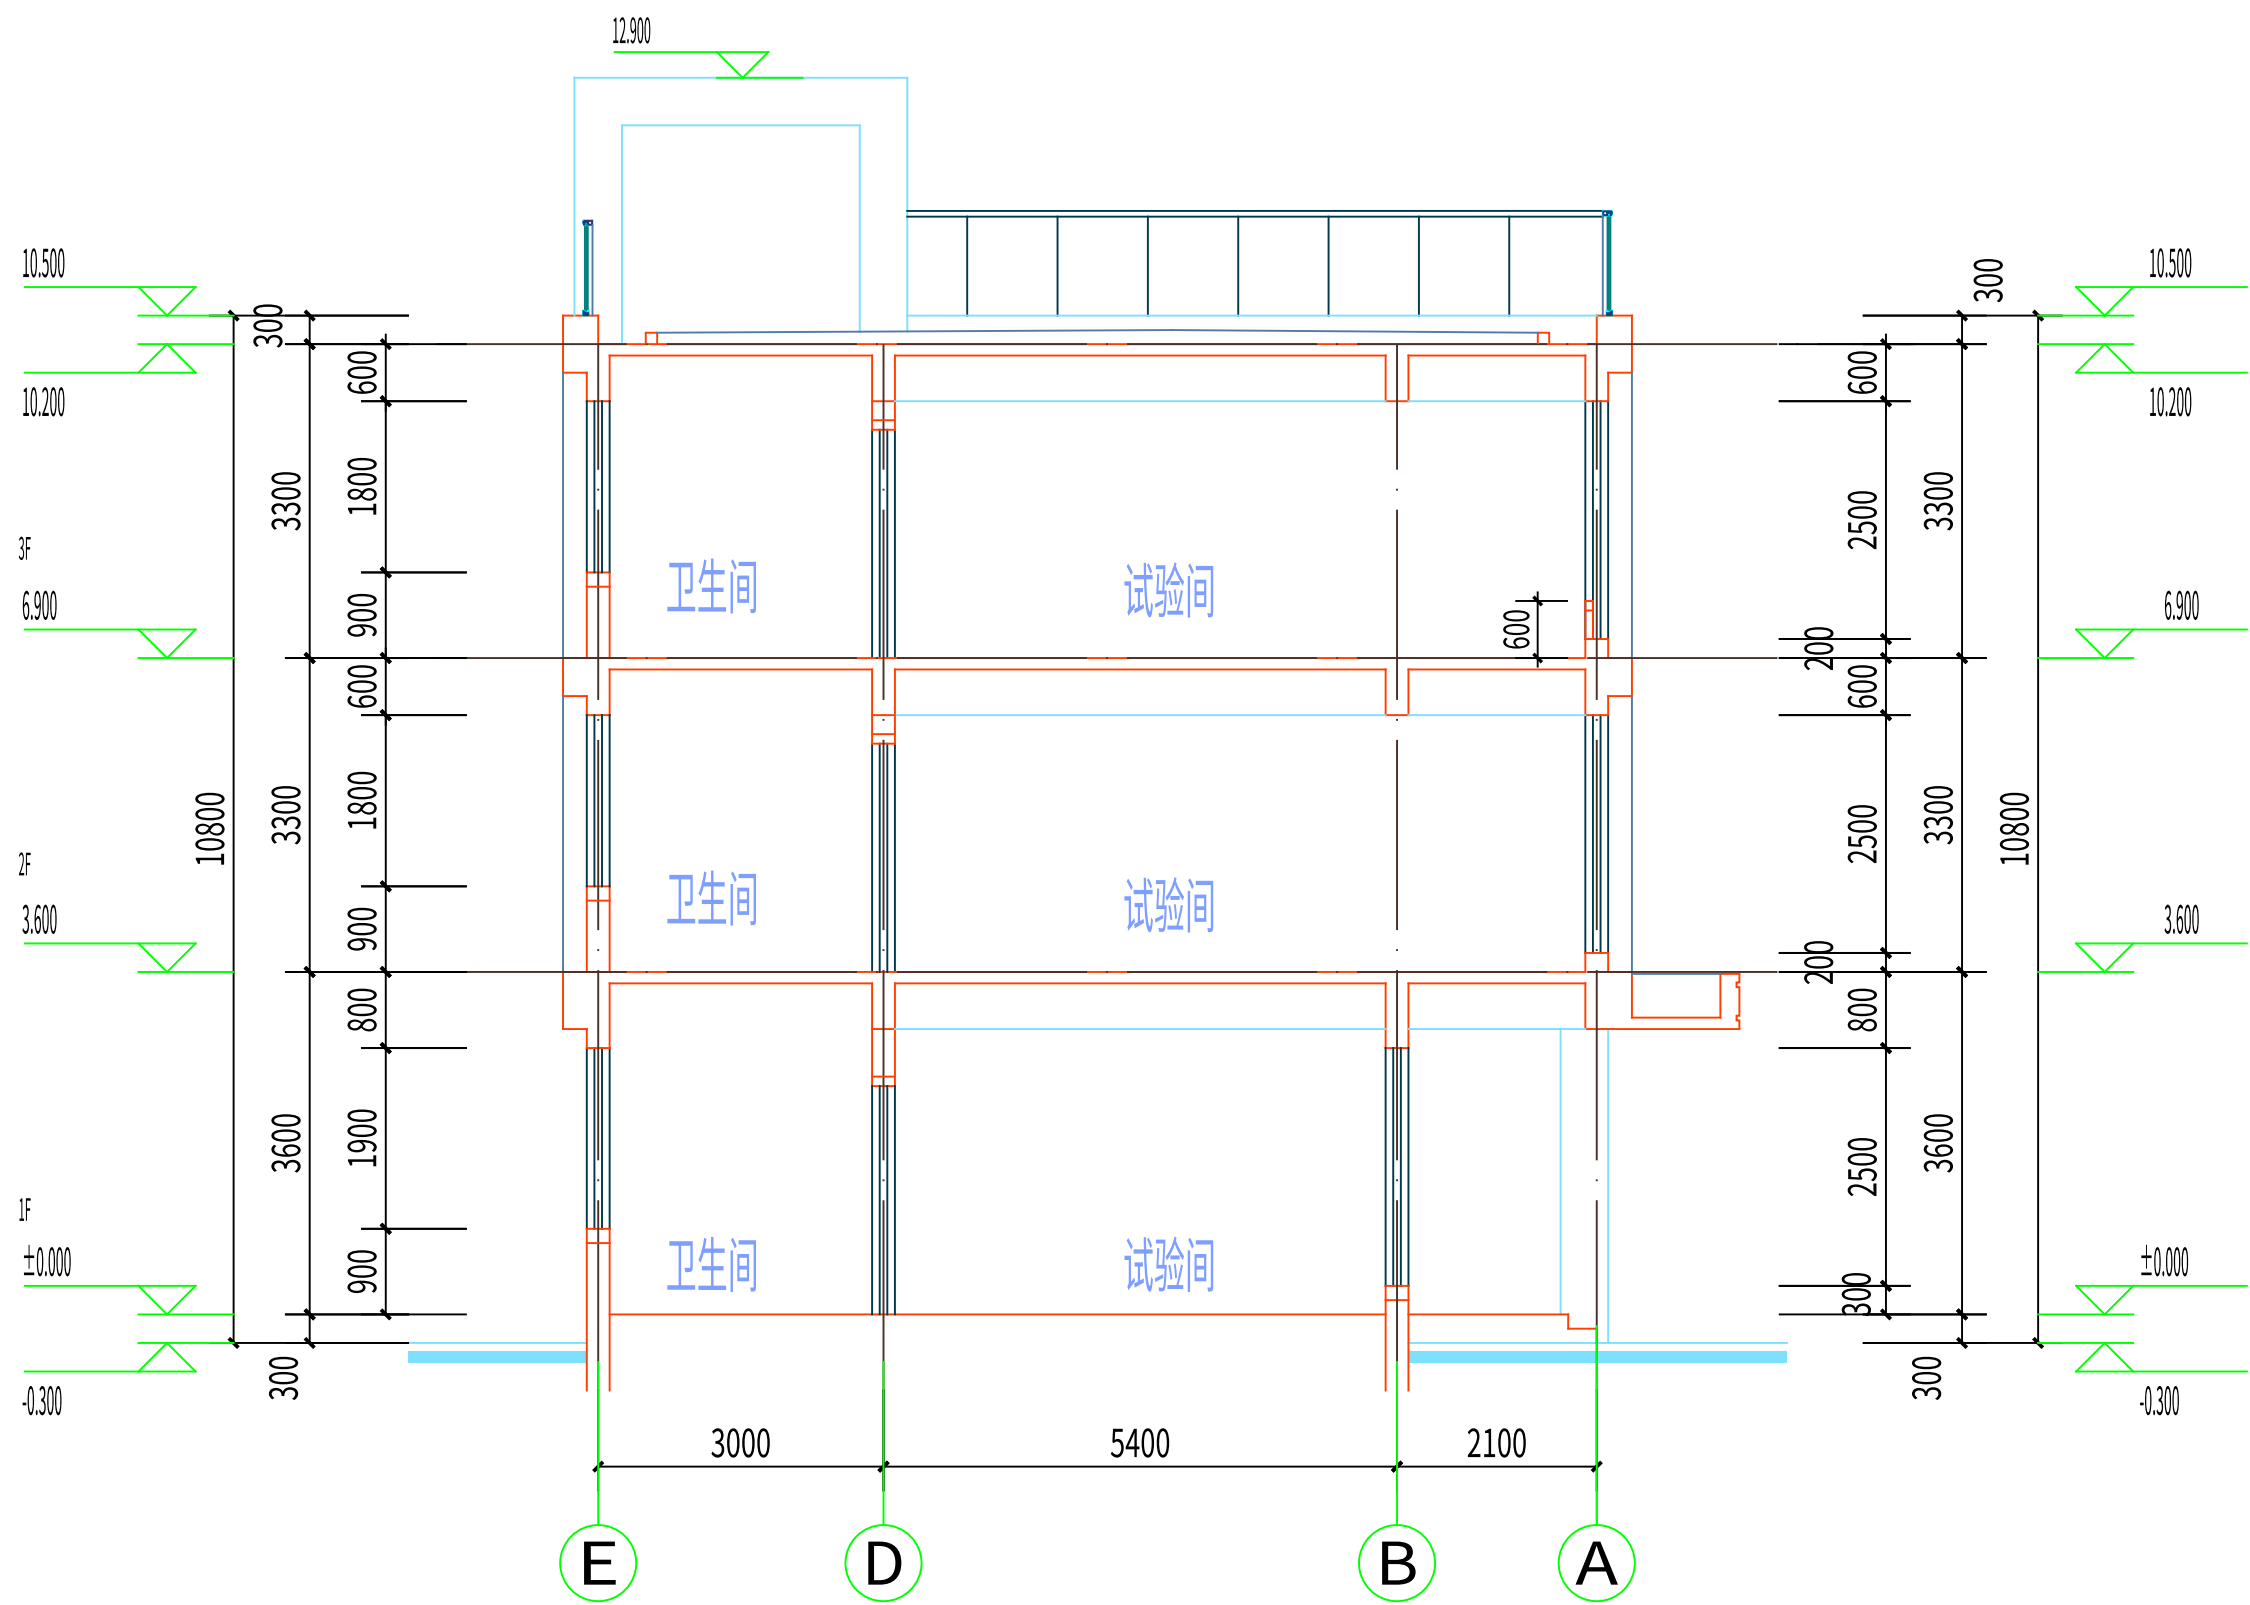


1-1 剖面图 1:100

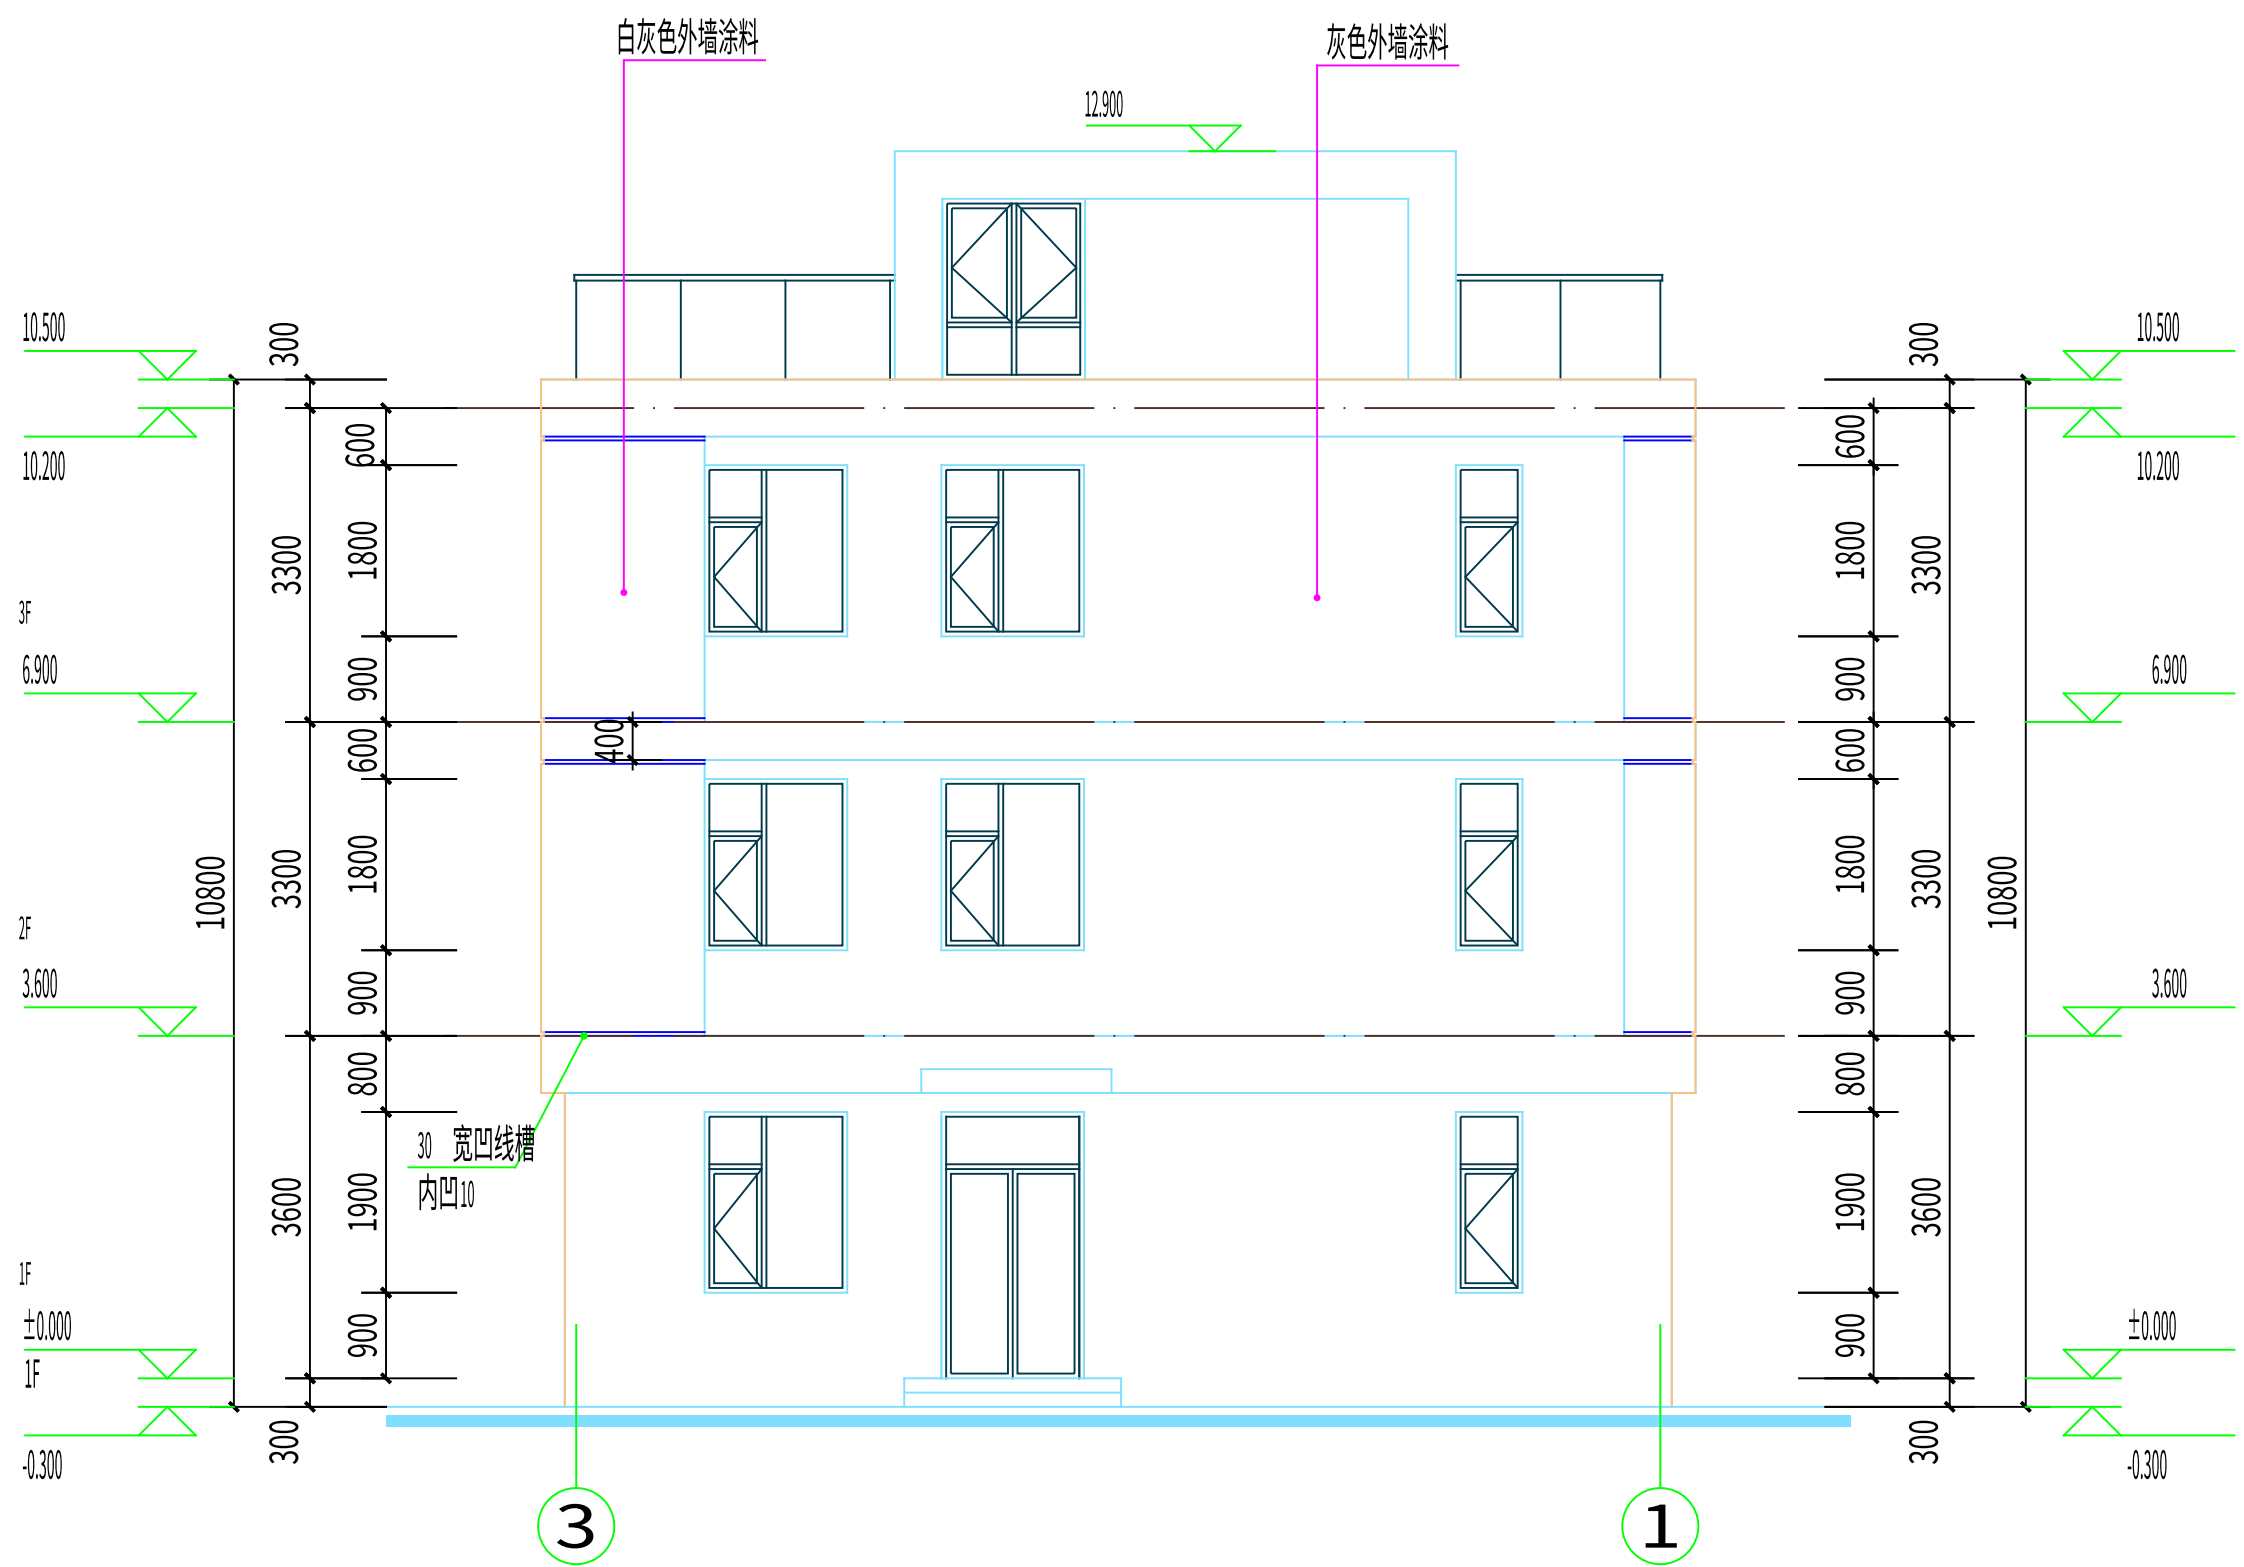


北立面图 1:100

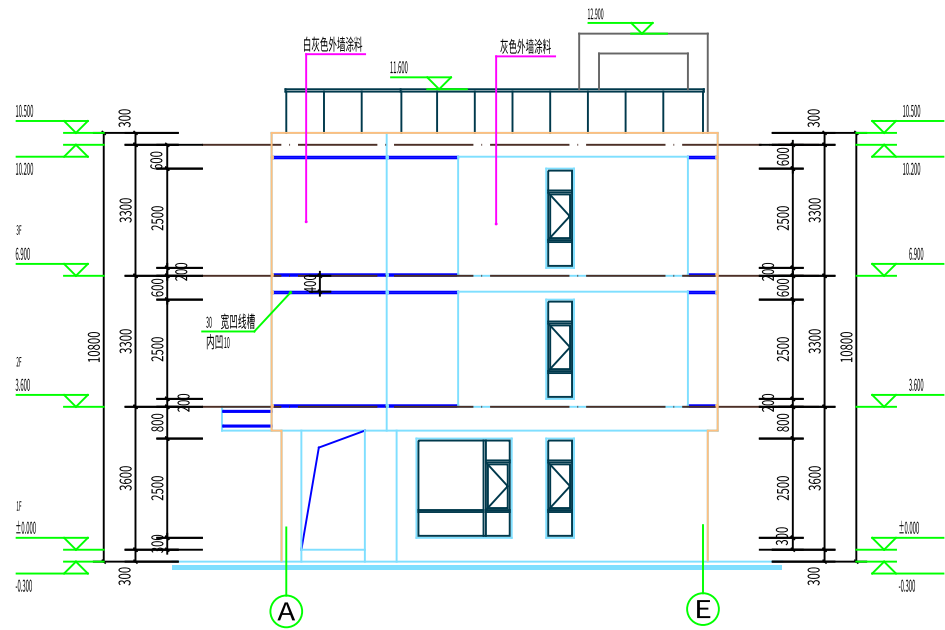

东立面图 1:100

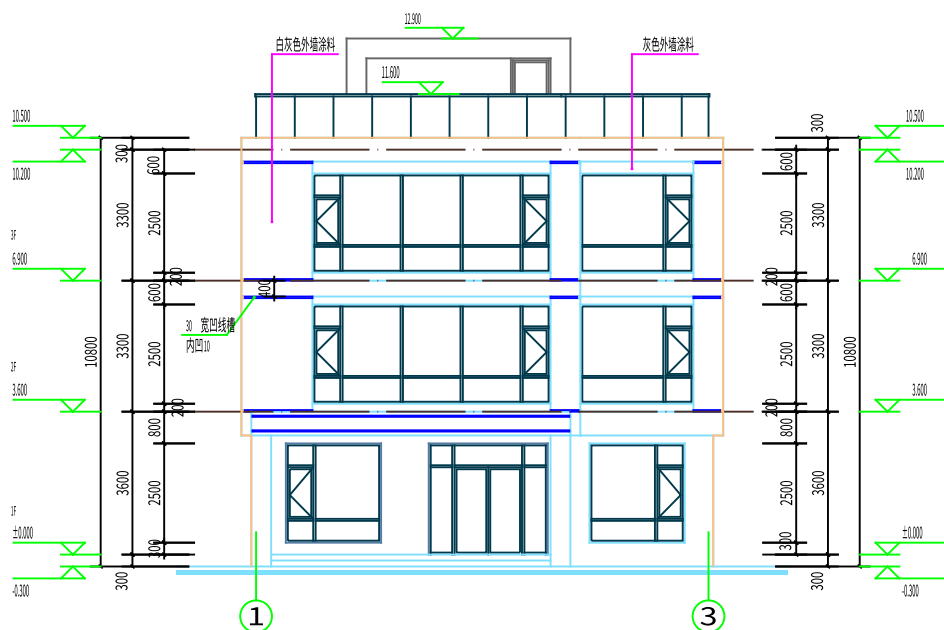

南立面图 1:100

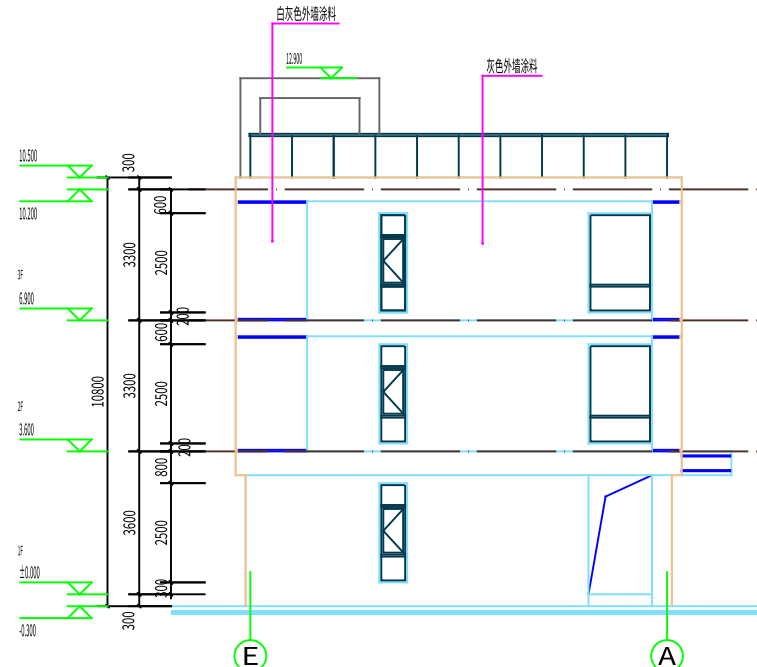

西立面图 1:100

- 消防救援口
- 消防救援口净高和净宽不小于1.0m
- 玻璃易于破碎, 并设置室外易于识别的明显标志

序号	图号	图名	图幅	备注
1	建施-0001	工程概况 门窗详图	A1	
2	建施-0002	一层平面图 二层平面图 三层平面图 屋顶平面图	A1	
3	建施-0003	东立面图 南立面图 西立面图 北立面图 1-1剖面图	A1	
4	建施-0004	1#楼梯详图 节点详图	A1	
		通用图		
5	建通施-0001	建筑施工图设计说明（一）	A1	
6	建通施-0002	建筑施工图设计说明（二）	A1	
7	建通施-0003	工程做法（一）	A1	
8	建通施-0004	工程做法（二）	A1	